ISOMÉTRICO AGUA POTABLE VIVIENDA

ESC:1/50

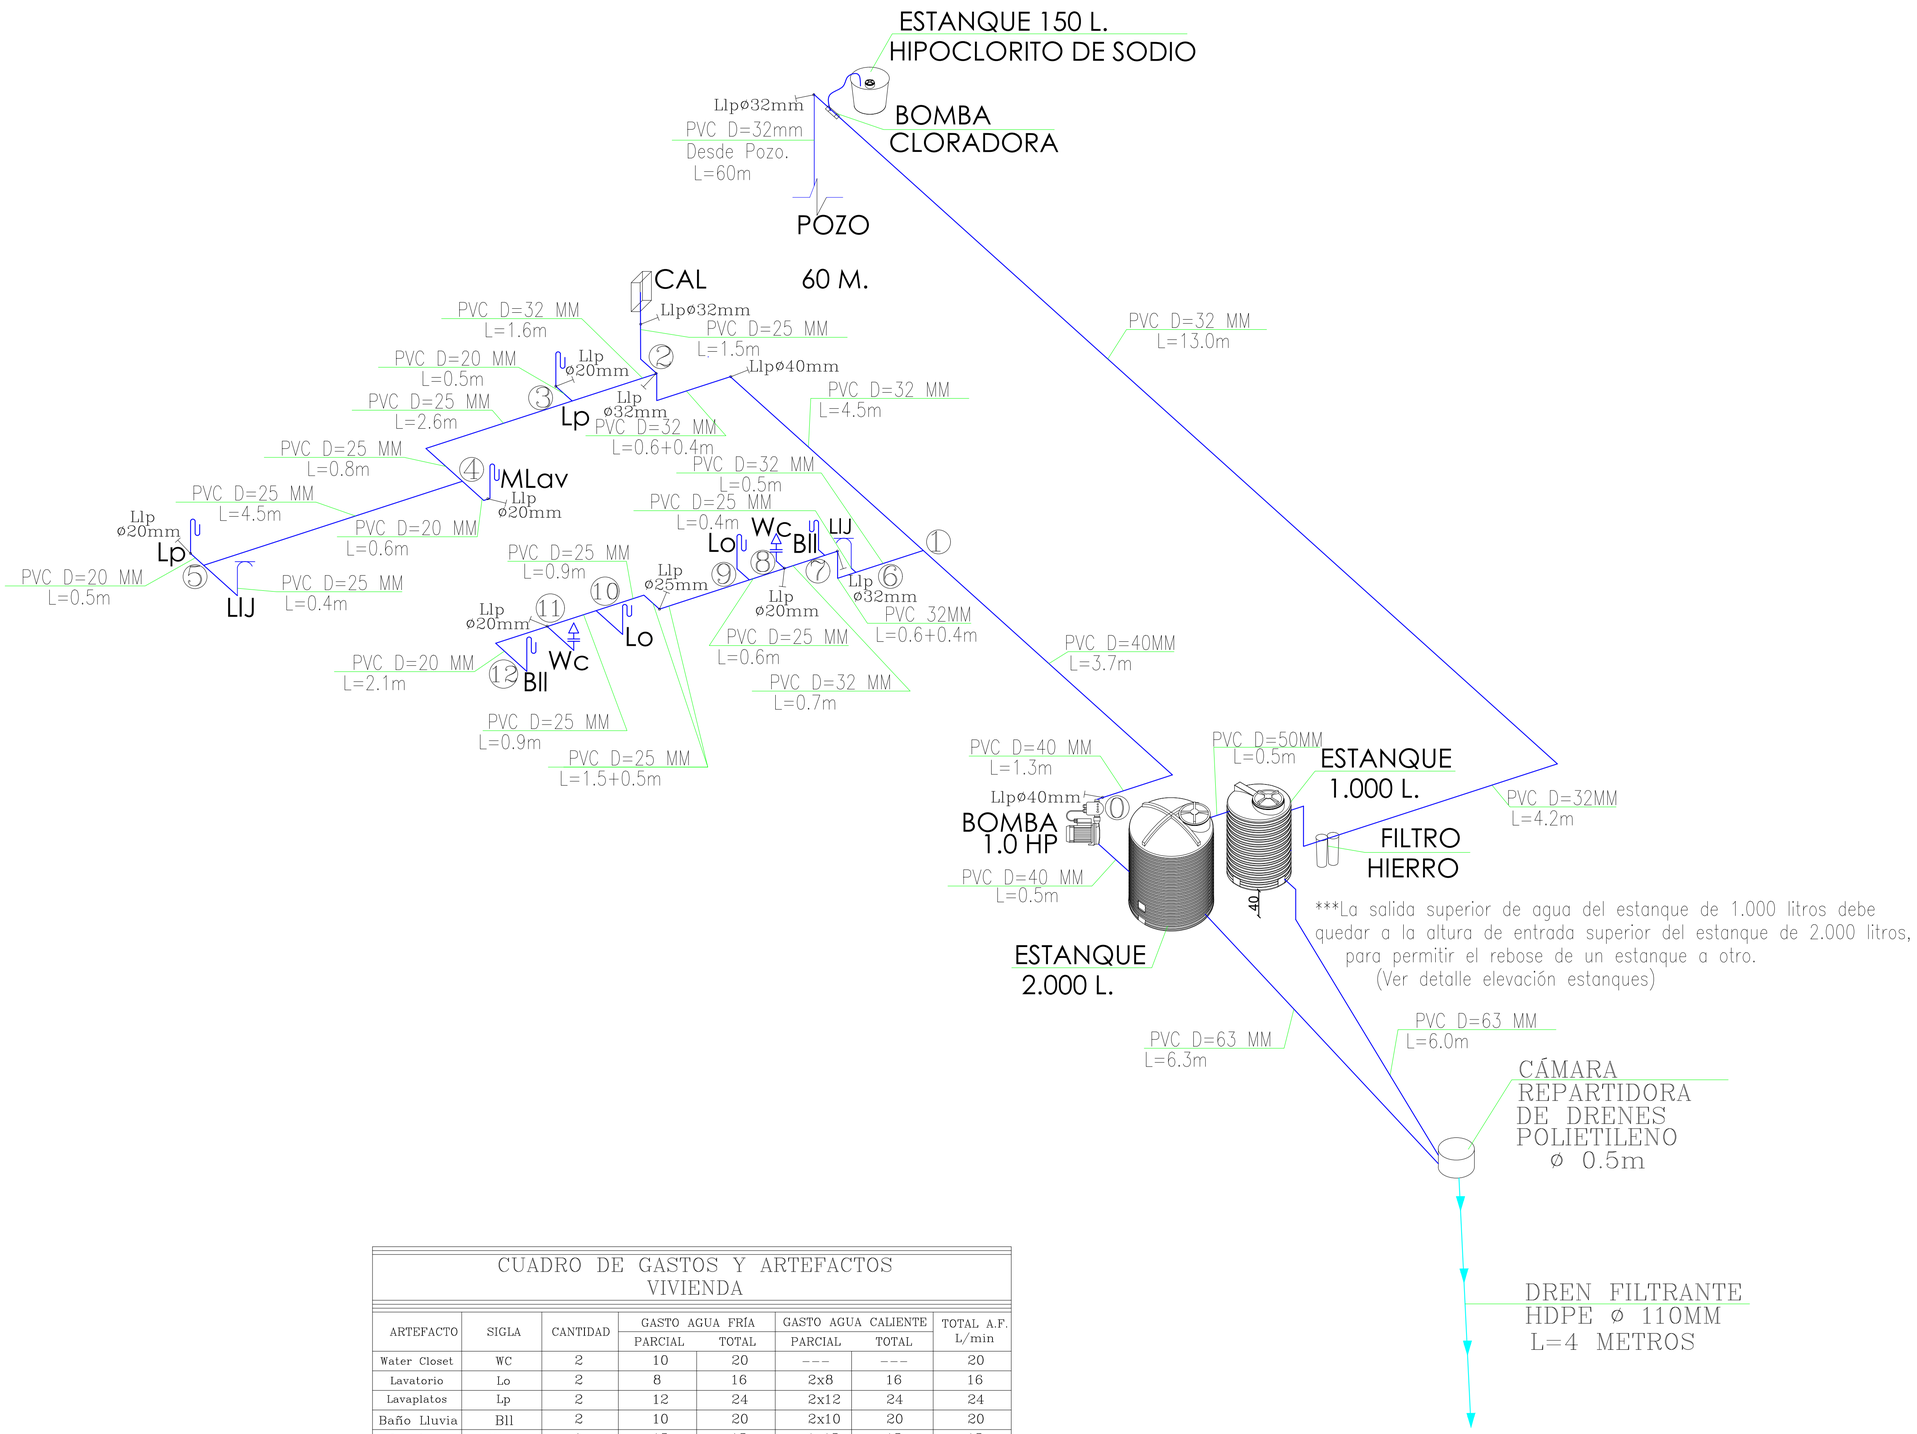

CUADRO DE GASTOS Y ARTEFACTOS VIVIENDA

ARTEFACTO	SIGLA	CANTIDAD	GASTO AGUA FRÍA		GASTO AGUA CALIENTE		TOTAL A.F. L/min
			PARCIAL	TOTAL	PARCIAL	TOTAL	
Water Closet	WC	2	10	20	---	---	20
Lavatorio	Lo	2	8	16	2x8	16	16
Lavaplatos	Lp	2	12	24	2x12	24	24
Baño Lluvia	Bll	2	10	20	2x10	20	20
Lavadora	MLav	1	15	15	1x15	15	15
Llave jardín	Llj	2	50	100	---	---	100
TOTAL		11		195		75/35	195/66
						Ql	195
						QMP	66

NOTAS IMPORTANTES

- Este proyecto no debe ser modificado sin las aprobaciones del Ingeniero Proyectista, Propietario y SEREMI de Salud.
- Obras proyectadas.

ÁREA: HIDRÁULICA

Ingeniería y Construcción
CABRER BESNIER SPA
jcbingenieriacivil@gmail.com FONO: +569 62402877

OBJETO: INSTALACIONES DOMICILIARIAS

PROYECTO N°	PLANO N°	PARTICIPANTES	DIA	MES	AÑO
		PROY: J. CABRER BESNIER			
		DIB: J. CABRER BESNIER			
ESCALA		REV: J. CABRER BESNIER			
INDICADAS		APR: J. CABRER BESNIER			
		IMPR: J. CABRER BESNIER			

RUTA:

LÁMINA 2 DE 5

MODIFICACIONES

EDICION	FECHA	MATERIA	APROBÓ
A		EMITIDO PARA REVISIÓN	

PROYECTO DE INSTALACIÓN DE ISOMÉTRICO AGUA POTABLE

PROYECTO INFORMATIVO

N° FECHA

AVISO DE INICIO N°

CERTIFICADO DE FACTIBILIDAD Nº

CALLE O PASAJE : SAN FRANCISCO DE TUNQUÉN N°419

LOTEO O POBLACIÓN : TUNQUÉN

NÚMERO MUNICIPAL : 419

ROL : 1290 - 58

COMUNA : ALGARROBO

UBICACIÓN

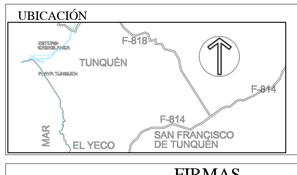

NOTAS ACLARATORIAS DE UBICACIÓN

Coordenadas de Ubicación
Latitud 33°17'59.6"S
Longitud 71°37'49.2"W

FIRMAS

PROYECTISTA

NOMBRE : JAVIER CABRER BESNIER
PROFESIÓN : INGENIERO CIVIL
RUT : 15.332.225-2
DOMICILIO : JANEQUEO #1510 CONCEPCIÓN

PROPIETARIO

NOMBRE : VÍCTOR NAZAR FUENTEALBA
RUT : 16.138.017-2
DOMICILIO : SAN FRANCISCO DE TUNQUÉN N°419 ALGARROBO

CONTRATISTA

NOMBRE :
PROFESIÓN :
RUT :
DOMICILIO :

PROYECTO DEFINITIVO
CERTIFICADO DE RECEPCIÓN

N° _____ FECHA _____

FIRMA SEREMI DE SALUD