EMPLAZAMIENTO Y RADIO DE PROTECCIÓN ALCANTARILLADO VIVIENDA

ESC:1/100

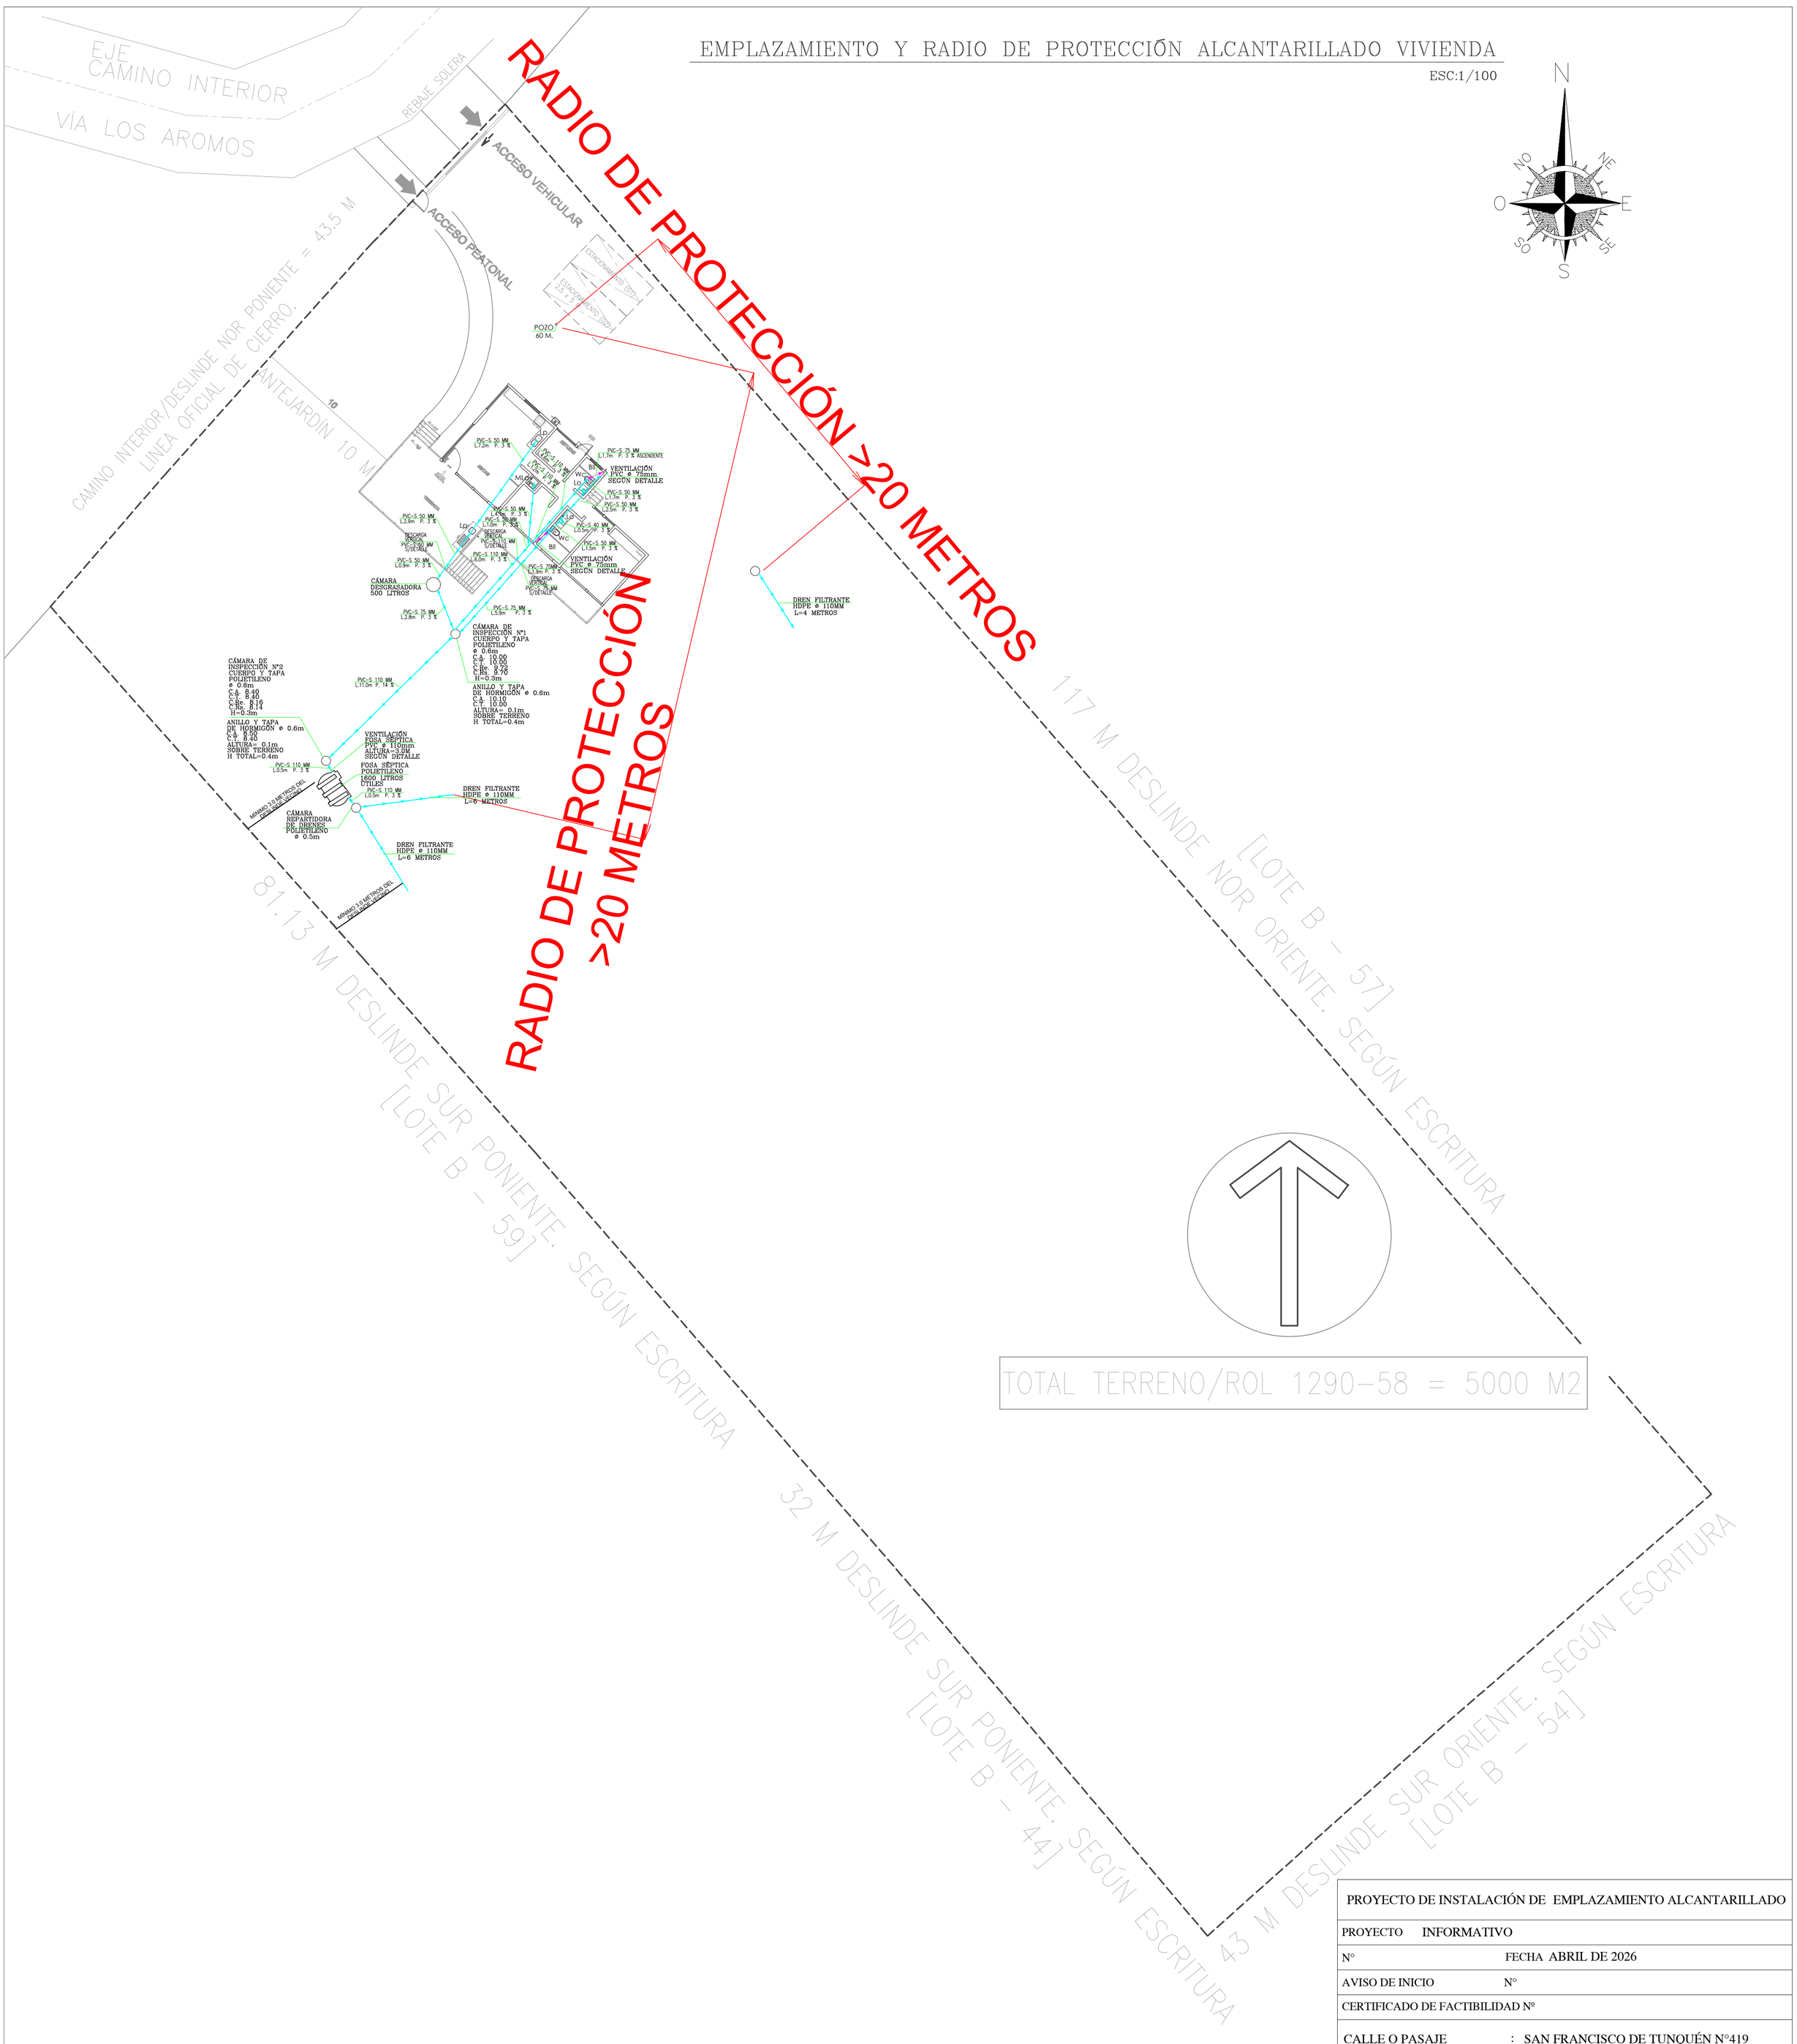

PROYECTO DE INSTALACIÓN DE EMPLAZAMIENTO ALCANTARILLADO	
PROYECTO	INFORMATIVO
N°	FECHA ABRIL DE 2026
AVISO DE INICIO	N°
CERTIFICADO DE FACTIBILIDAD Nº	

CALLE O PASAJE	:	SAN FRANCISCO DE TUNQUÉN N°419
LOTEO O POBLACIÓN	:	TUNQUÉN
NÚMERO MUNICIPAL	:	419
ROL	:	1290 - 58
COMUNA	:	ALGARROBO

UBICACIÓN

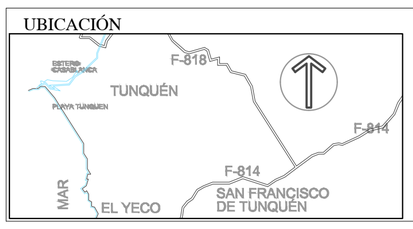

NOTAS ACLARATORIAS DE UBICACIÓN

Coordenadas de Ubicación
Latitud 33°17'59.6"S
Longitud 71°37'49.2"W

ÁREA
HIDRÁULICA

Ingeniería y Construcción
CABRER BESNIER SPA
jcbingenieriacivil@gmail.com FONO: +569 62402877

OBJETO
INSTALACIONES DOMICILIARIAS

PROYECTO N° PLANO N°

ESCALA
INDICADAS

PARTICIPANTES	DIA	MES	AÑO
PROY: J. CABRER BESNIER			
DIB: J. CABRER BESNIER			
REV: J. CABRER BESNIER			
APR: J. CABRER BESNIER			
IMPR: J. CABRER BESNIER			

RUTA:

LÁMINA 4 DE 4

MODIFICACIONES

EDICION	FECHA	MATERIA	APROBÓ
A		EMITIDO PARA REVISIÓN	

NOTAS IMPORTANTES

- Este proyecto no debe ser modificado sin las aprobaciones del Ingeniero Proyectista, Propietario y SEREMI de Salud.
- Obras proyectadas.
- NPT = Nivel de piso terminado.
- CT = Cota de terreno.

FIRMAS

PROYECTISTA

NOMBRE : JAVIER CABRER BESNIER
PROFESIÓN : INGENIERO CIVIL
RUT : 15.332.225-2
DOMICILIO : JANEQUEO #1510 CONCEPCIÓN

PROPIETARIO

NOMBRE : VÍCTOR NAZAR FUENTEALBA
RUT : 16.138.017-2
DOMICILIO : SAN FRANCISCO DE TUNQUÉN N°419 ALGARROBO

CONTRATISTA

NOMBRE :
PROFESIÓN :
RUT :
DOMICILIO :

PROYECTO DEFINITIVO
CERTIFICADO DE RECEPCIÓN

N° _____ FECHA _____

FIRMA SEREMI DE SALUD