ISOMÉTRICO ALCANTARILLADO VIVIENDA

ESC:1/50

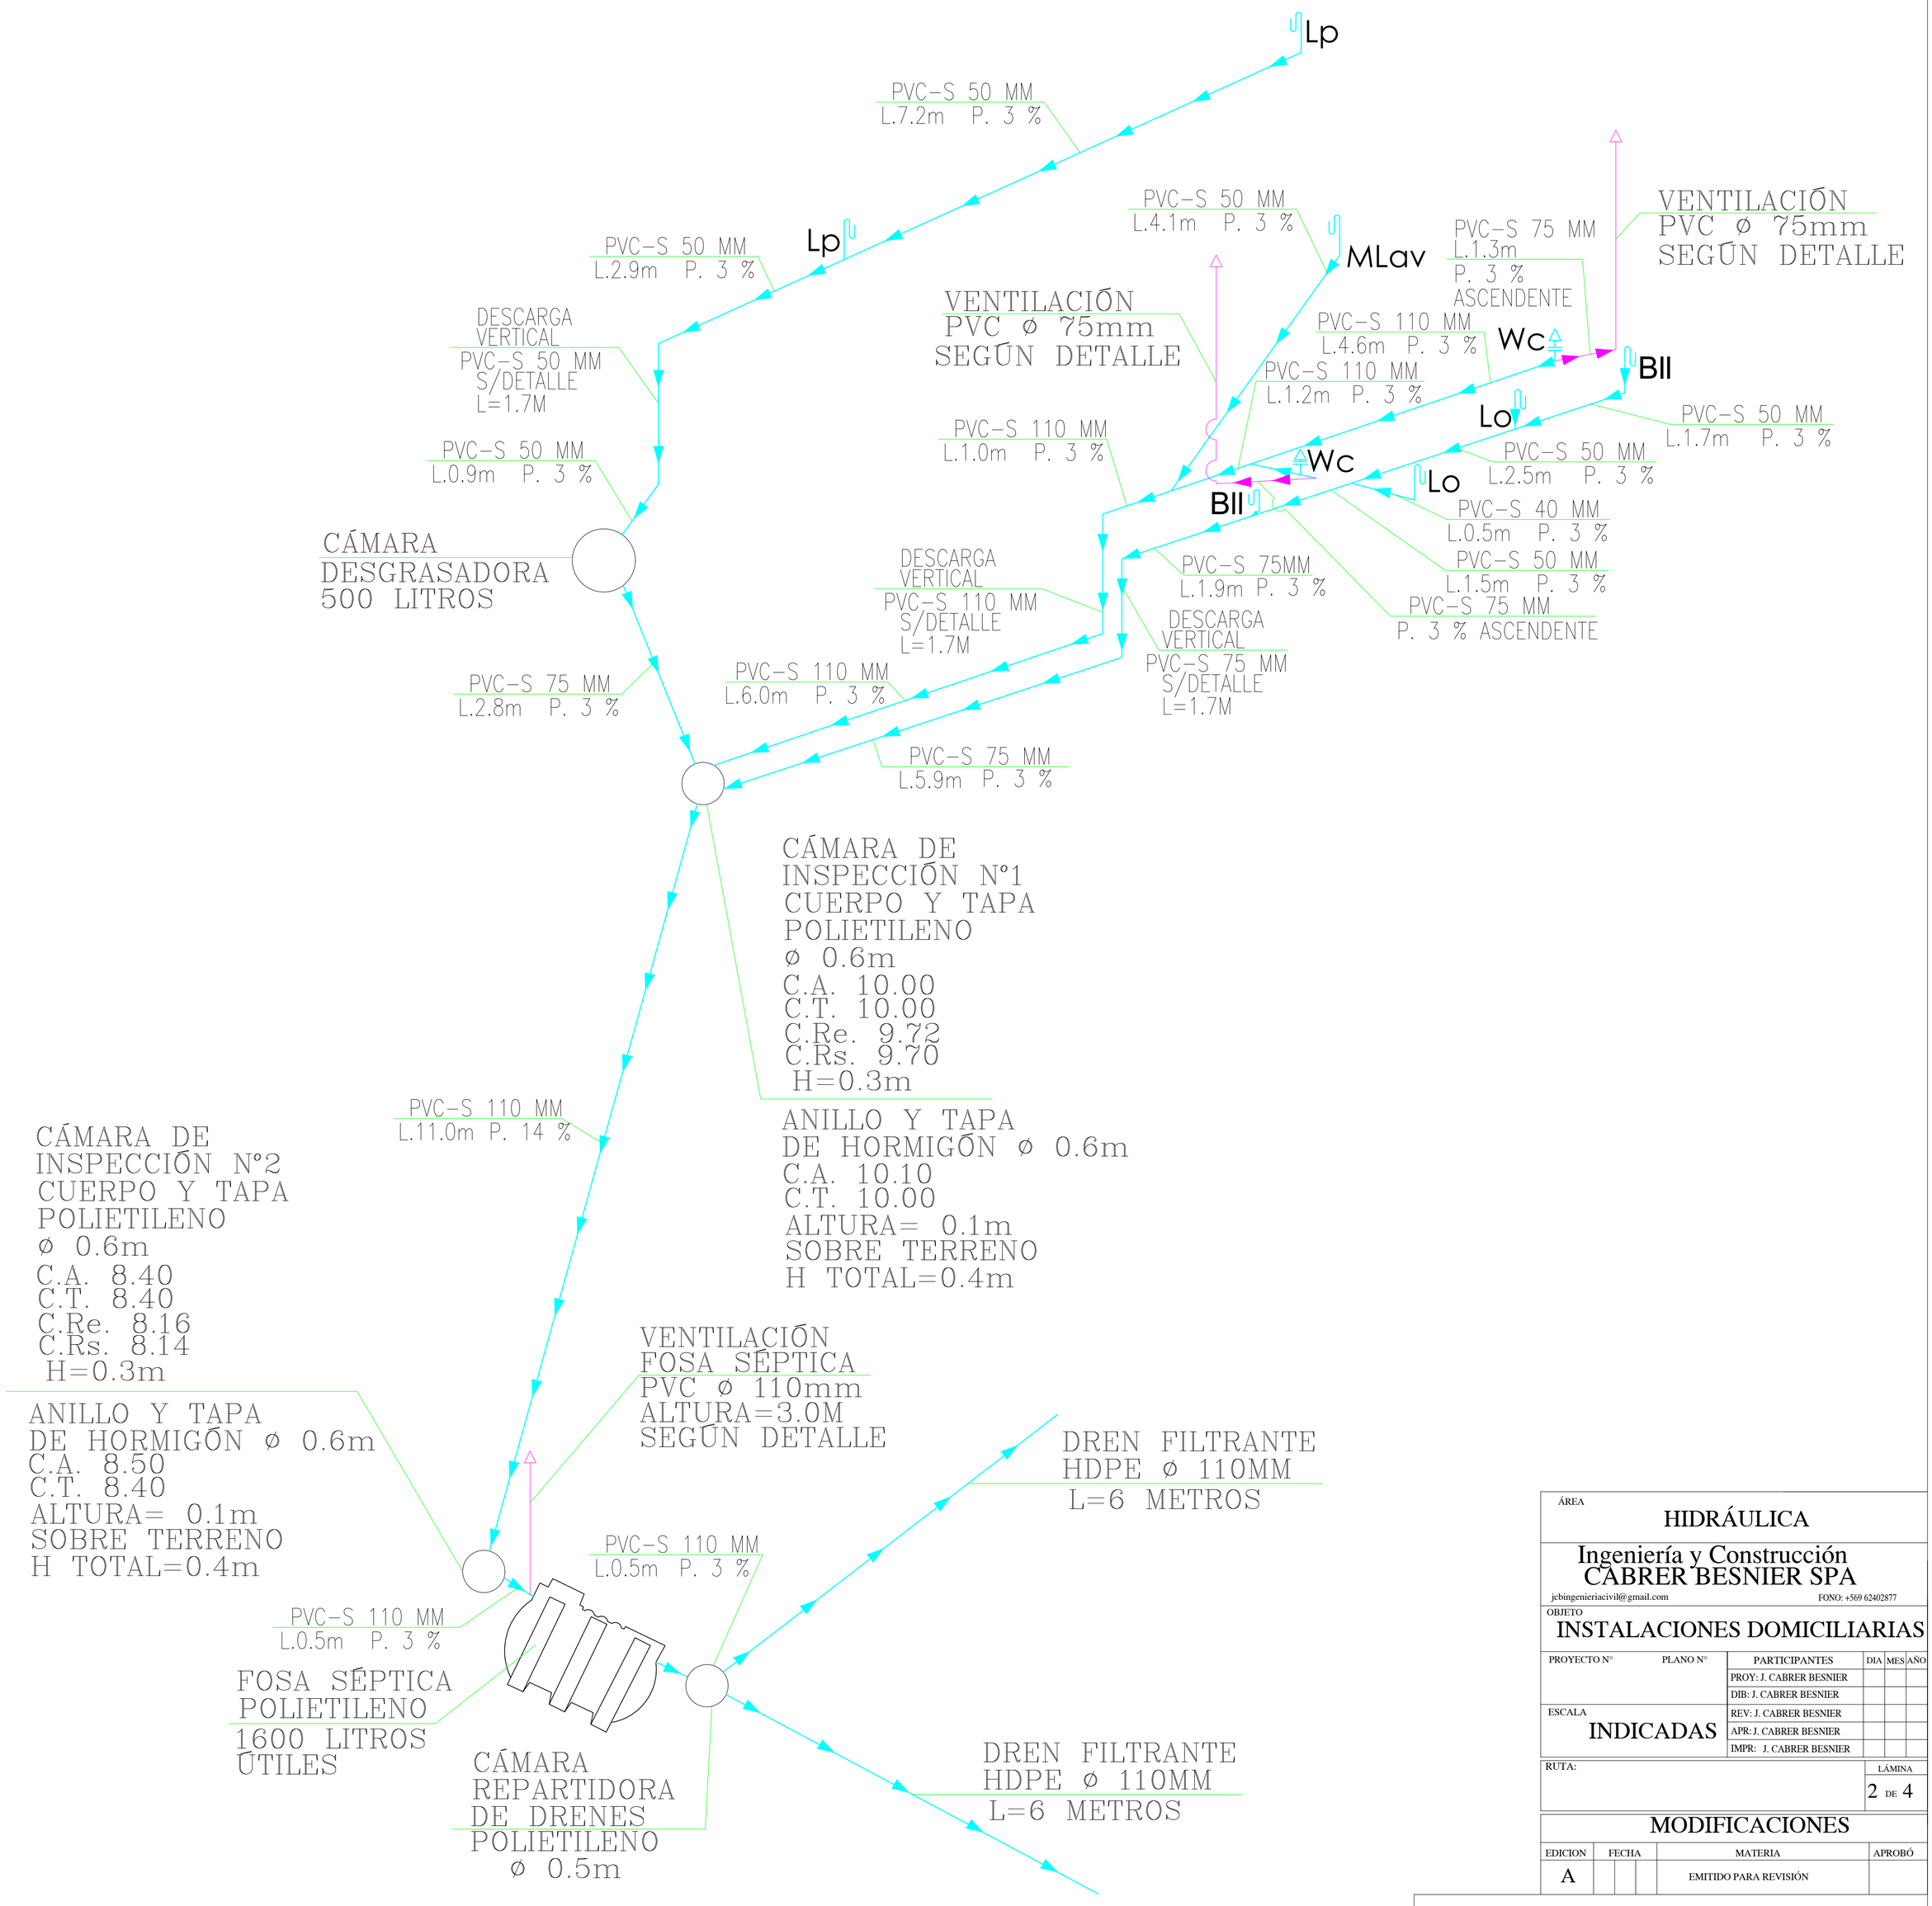

CUADRO DE UEH SISTEMA

ARTEFACTO	SIGLA	CANTIDAD	CLASE	UEH	TOTAL
Water Closet	WC	2	1	3	6
Lavatorio	Lo	2	1	1	2
Lavaplatos	Lp	2	1	3	6
Baño Lluvia	Bll	2	1	2	4
Lavadora	MLav	1	1	3	3
TOTAL		9			21

NOTAS IMPORTANTES

- Este proyecto no debe ser modificado sin las aprobaciones del Ingeniero Proyectista, Propietario y SEREMI de Salud.
- Obras proyectadas.
- NPT = Nivel de piso terminado.
- CT = Cota de terreno.

ÁREA
HIDRÁULICA

Ingeniería y Construcción
CABRER BESNIER SPA
jcbingenieriacivil@gmail.com FONO: +569 62402877

OBJETO
INSTALACIONES DOMICILIARIAS

PROYECTO N°	PLANO N°	PARTICIPANTES	DIA	MES	AÑO
		PROY: J. CABRER BESNIER			
		DIB: J. CABRER BESNIER			
ESCALA INDICADAS		REV: J. CABRER BESNIER			
		APR: J. CABRER BESNIER			
		IMPR: J. CABRER BESNIER			

RUTA:

LÁMINA 2 DE 4

MODIFICACIONES

EDICION	FECHA	MATERIA	APROBÓ
A		EMITIDO PARA REVISIÓN	

PROYECTO DE INSTALACIÓN DE ISOMÉTRICO ALCANTARILLADO

PROYECTO INFORMATIVO

N° FECHA

AVISO DE INICIO N°

CERTIFICADO DE FACTIBILIDAD Nº

CALLE O PASAJE : SAN FRANCISCO DE TUNQUÉN N°419
LOTEO O POBLACIÓN : TUNQUÉN
NÚMERO MUNICIPAL : 419
ROL : 1290 - 58
COMUNA : ALGARROBO

UBICACIÓN

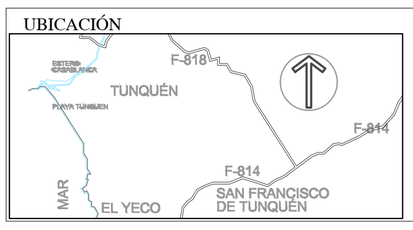

NOTAS ACLARATORIAS DE UBICACIÓN

Coordenadas de Ubicación
Latitud 33°17'59.6"S
Longitud 71°37'49.2"W

FIRMAS

PROYECTISTA
NOMBRE : JAVIER CABRER BESNIER
PROFESIÓN : INGENIERO CIVIL
RUT : 15.332.225-2
DOMICILIO : JANEQUEO #1510 CONCEPCIÓN

PROPIETARIO
NOMBRE : VÍCTOR NAZAR FUENTEALBA
RUT : 16.138.017-2
DOMICILIO : SAN FRANCISCO DE TUNQUÉN N°419 ALGARROBO

CONTRATISTA
NOMBRE :
PROFESIÓN :
RUT :
DOMICILIO :

PROYECTO DEFINITIVO
CERTIFICADO DE RECEPCIÓN
N° _____ FECHA _____

FIRMA SEREMI DE SALUD