PLANTA ALCANTARILLADO VIVIENDA

ESC:1/50

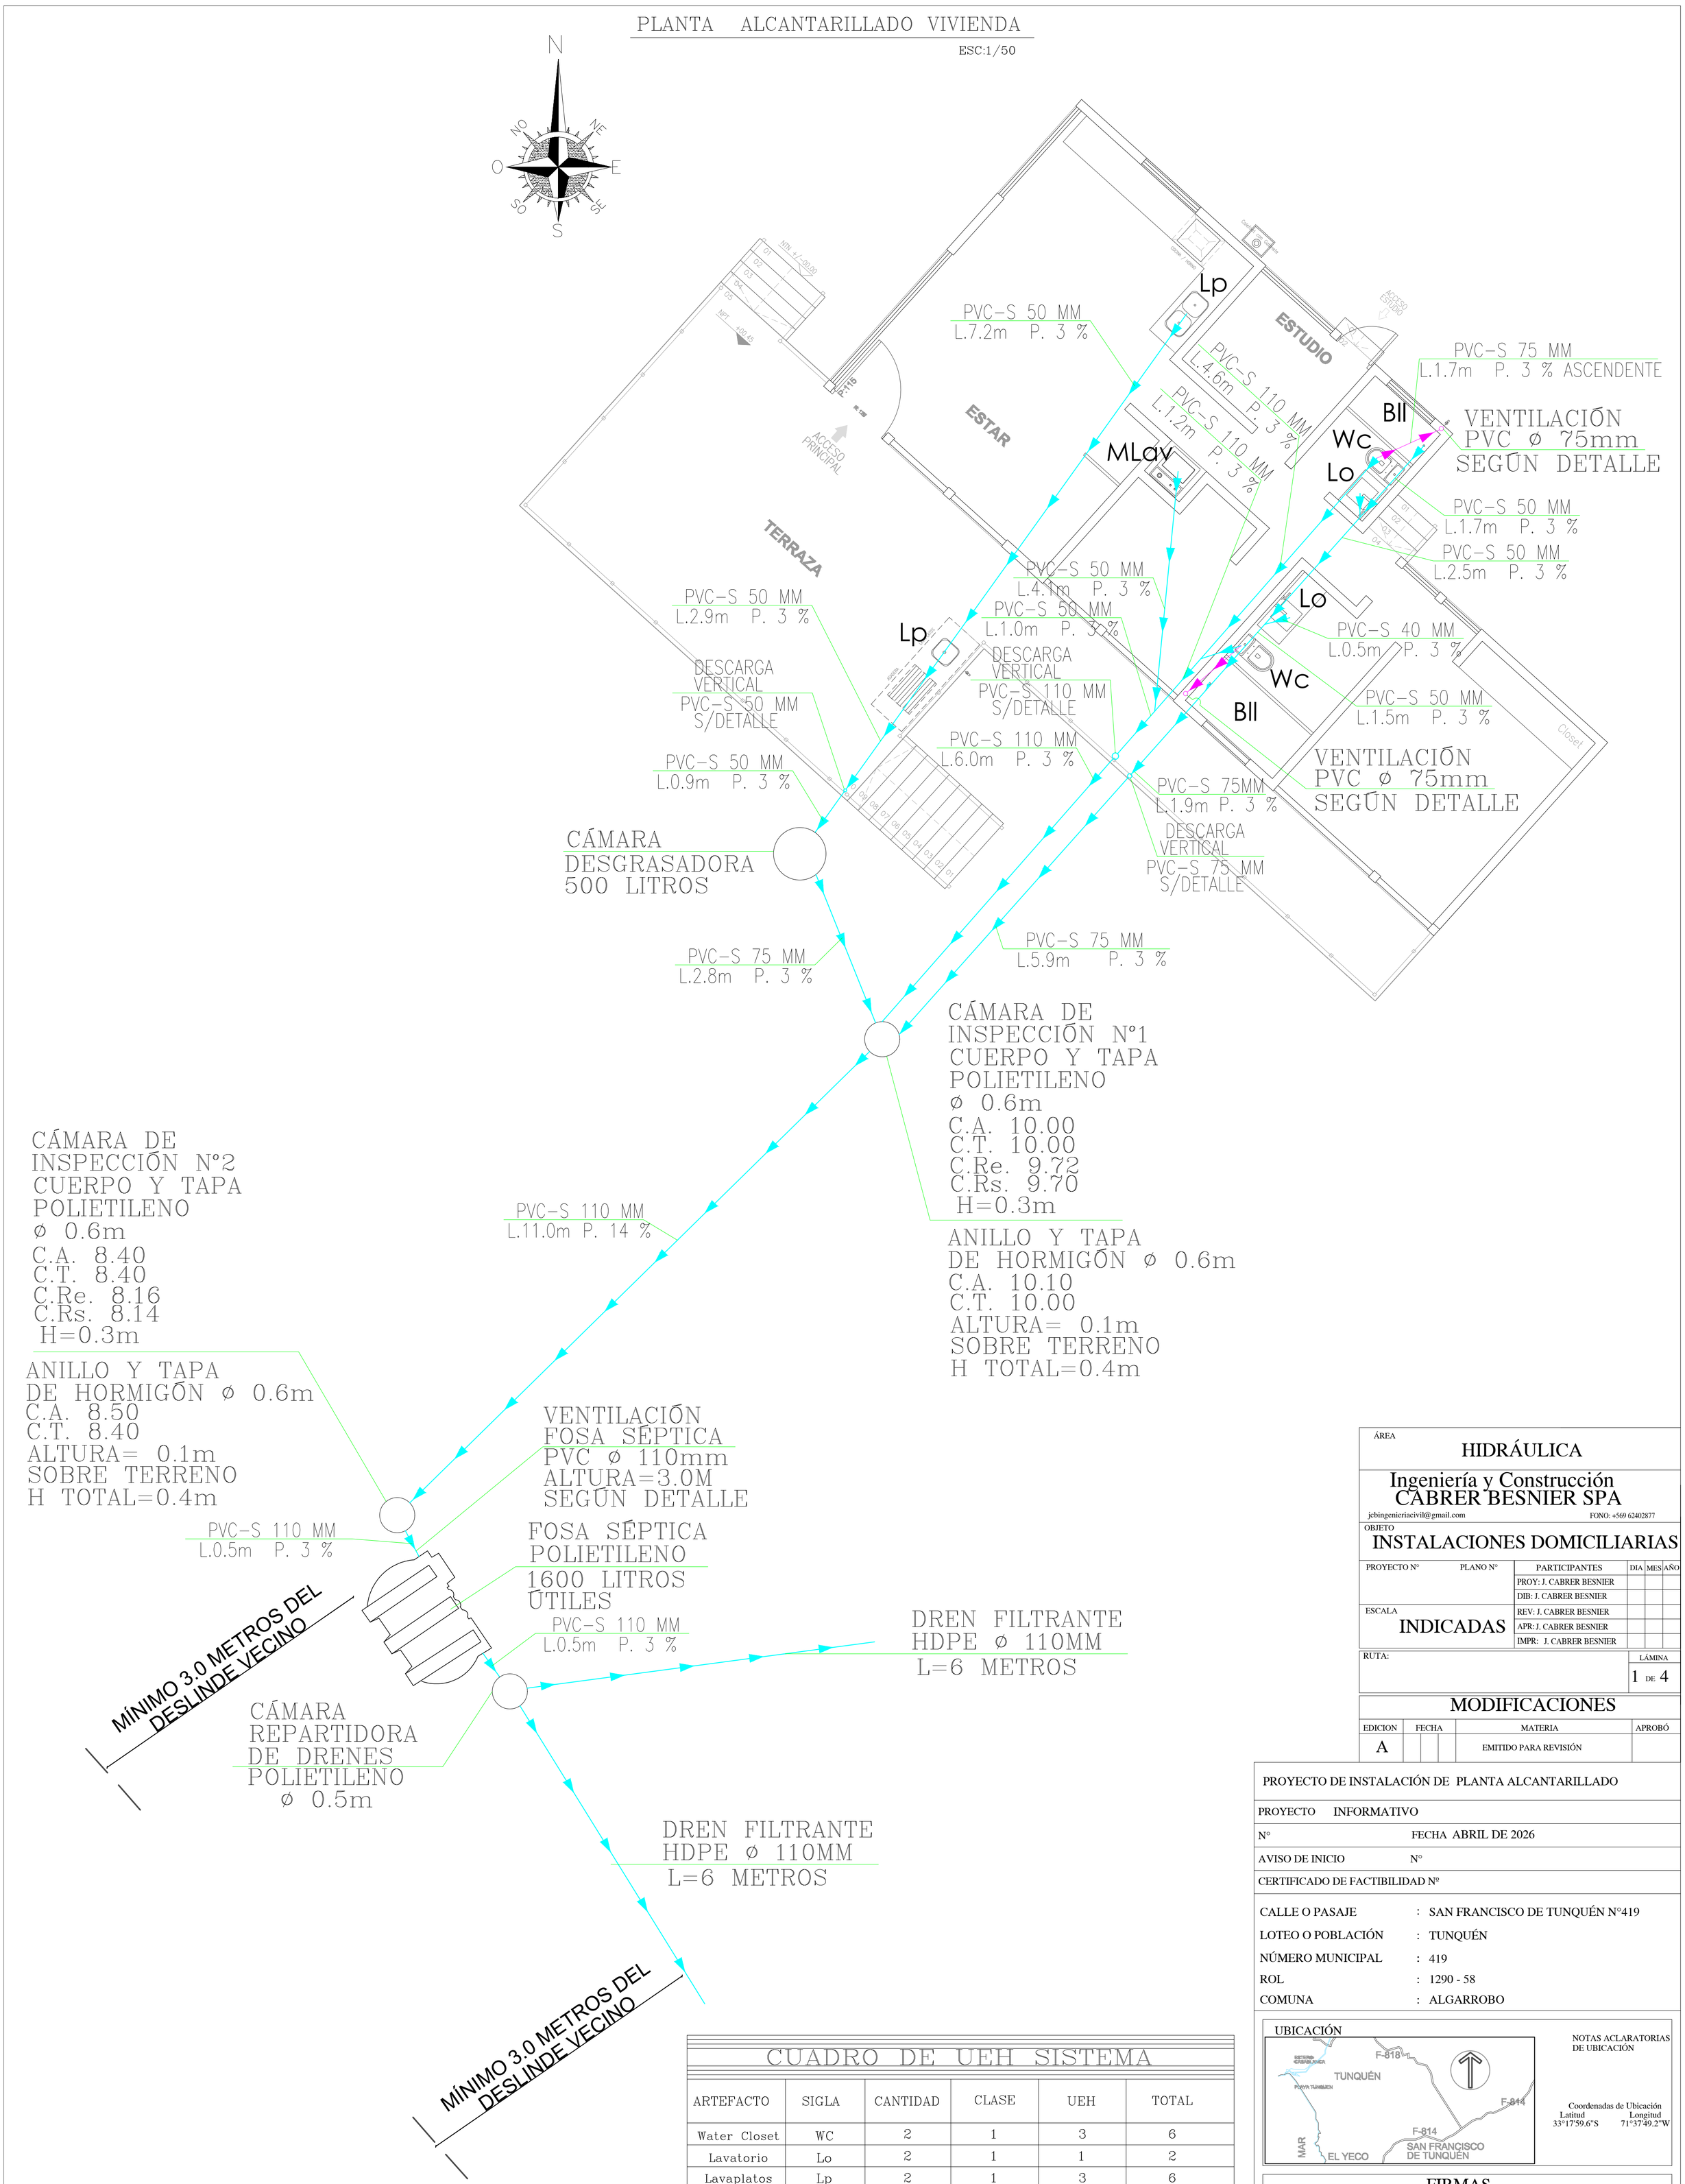

CUADRO DE UEH SISTEMA

ARTEFACTO	SIGLA	CANTIDAD	CLASE	UEH	TOTAL
Water Closet	WC	2	1	3	6
Lavatorio	Lo	2	1	1	2
Lavaplatos	Lp	2	1	3	6
Baño Lluvia	Bll	2	1	2	4
Lavadora	MLav	1	1	3	3
TOTAL		9			21

NOTAS IMPORTANTES

- Este proyecto no debe ser modificado sin las aprobaciones del Ingeniero Proyectista, Propietario y SEREMI de Salud.
- Obras proyectadas.
- NPT = Nivel de piso terminado.
- CT = Cota de terreno.

ÁREA: HIDRÁULICA

Ingeniería y Construcción CABRER BESNIER SPA

jcbingenieriacivil@gmail.com FONO: +569 62402877

OBJETO: INSTALACIONES DOMICILIARIAS

PROYECTO N° PLANO N°

PARTICIPANTES	DIA	MES	AÑO
PROY: J. CABRER BESNIER			
DIB: J. CABRER BESNIER			
REV: J. CABRER BESNIER			
APR: J. CABRER BESNIER			
IMPR: J. CABRER BESNIER			

ESCALA: INDICADAS

RUTA:

LÁMINA 1 DE 4

MODIFICACIONES

EDICION	FECHA	MATERIA	APROBÓ
A		EMITIDO PARA REVISIÓN	

PROYECTO DE INSTALACIÓN DE PLANTA ALCANTARILLADO

PROYECTO INFORMATIVO

N° FECHA ABRIL DE 2026

AVISO DE INICIO N°

CERTIFICADO DE FACTIBILIDAD Nº

CALLE O PASAJE : SAN FRANCISCO DE TUNQUÉN N°419

LOTEO O POBLACIÓN : TUNQUÉN

NÚMERO MUNICIPAL : 419

ROL : 1290 - 58

COMUNA : ALGARROBO

UBICACIÓN

NOTAS ACLARATORIAS DE UBICACIÓN

Coordenadas de Ubicación
Latitud 33°17'59.6"S
Longitud 71°37'49.2"W

FIRMAS

PROYECTISTA

NOMBRE : JAVIER CABRER BESNIER
PROFESIÓN : INGENIERO CIVIL
RUT : 15.332.225-2
DOMICILIO : JANEQUEO #1510 CONCEPCIÓN

PROPIETARIO

NOMBRE : VÍCTOR NAZAR FUENTEALBA
RUT : 16.138.017-2
DOMICILIO : SAN FRANCISCO DE TUNQUÉN N°419 ALGARROBO

CONTRATISTA

NOMBRE :
PROFESIÓN :
RUT :
DOMICILIO :

PROYECTO DEFINITIVO CERTIFICADO DE RECEPCIÓN

N° FECHA

FIRMA SEREMI DE SALUD